



1
A–1
PERSPECTIVE
NTS

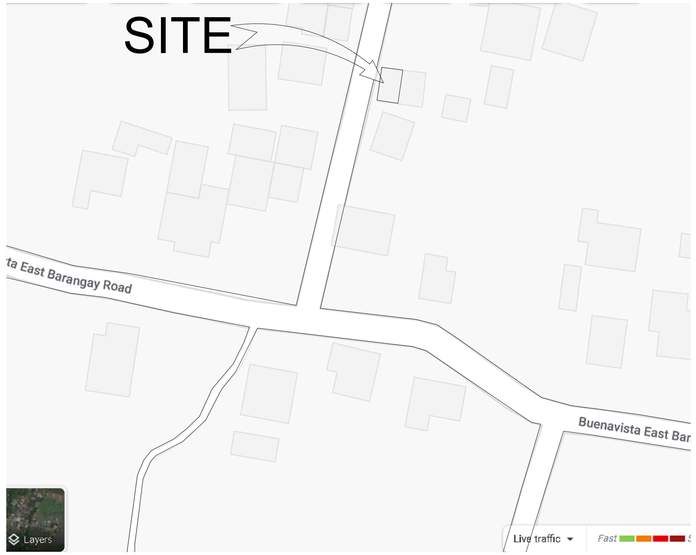

2
A–1
LOCATION PLAN
NTS

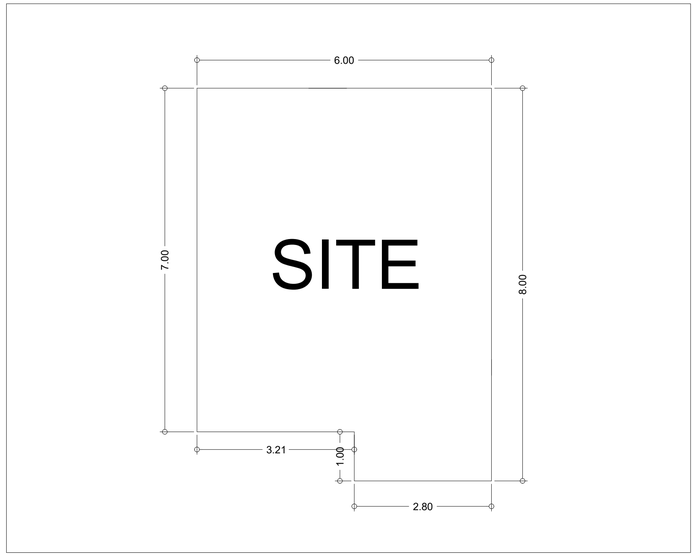

3
A–1
SITE DEVELOPMENT
NTS

Republic of the Philippines
Department of Public Works
Transportation and Communications
OFFICE OF THE BUILDING OFFICIAL

DISTRICT/CITY MUNICIPALITY

LAND USE AND ZONING

LINE AND GRADE

ARCHITECTURAL

CIVIL/STRUCTURAL

ELECTRICAL

SANITARY

PLUMBING

TABLE OF CONTENT

A-1	PERSPECTIVE,SITE DEVELOPMENT PLAN , LOCATION PLAN & TABLE OF CONTENT
A-2	GF ,2ND & ROOFDECK FLOOR PLAN
A-3	FRONT , REAR & RIGHT ELEVATION
E-1	LIGHTNING & POWER LAYOUT
P-1	SANITARY & WATERLINE LAYOUT

DESIGN CONSULTANT: ARCHITECT		DESIGN CONSULTANT: ENGINEER	
PTR NO.	REG. NO.	PTR NO.	REG. NO.
ISSUED ON	TIN.	ISSUED ON	TIN.
PLACE		PLACE	

DESIGN BY:
CHECKED BY:
DRAWN BY: MCPB
DATE:

IMPORTANT:
THESE DRAWINGS ARE INTELLECTUAL PROPRIETARY RIGHTS RETAINED BY DESIGNER OVER ANY DESIGNERS DOCUMENTS UNLESS THERE IS A WRITTEN STIPULATION TO THE CONTRARY. COPYRIGHT IN A WORK OF DESIGNER.
(RA 544)

PROJECT:
PROPOSED TWO-STOREY RESIDENTIAL W/ ROOFDECK
LOCATION :


OWNER

SHEET CONTENTS:


REVISIONS:

SHEET NO: A-1


☐ DESIGN DEVELOPMENT ■ FOR PERMIT PLAN ☐ FOR CONSTRUCTION PLAN ☐ ADDENDUM PLAN ☐ AS-BUILT PLAN

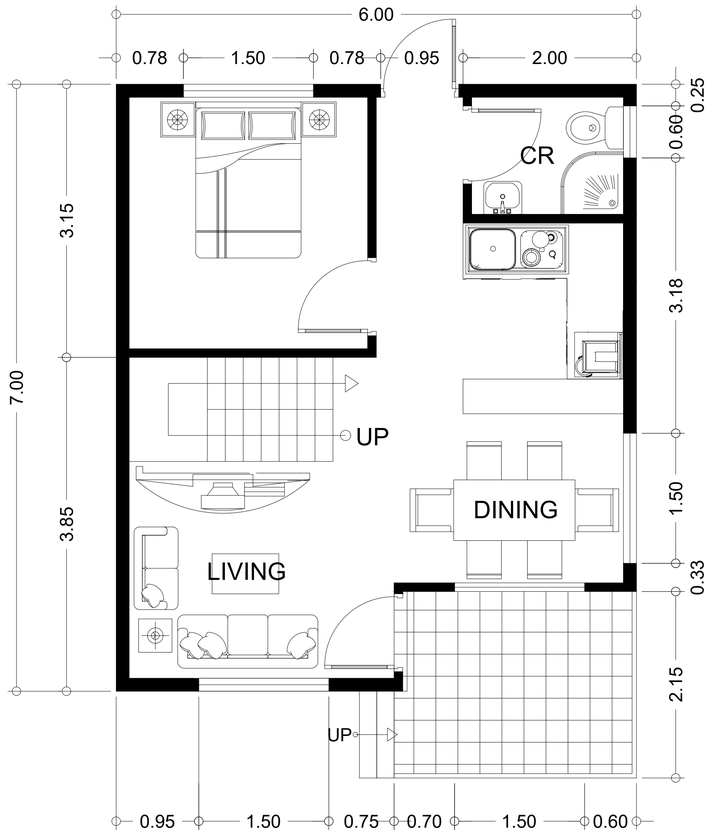

1 A–2 GROUND FLOOR PLAN
SCALE 1:75MTS

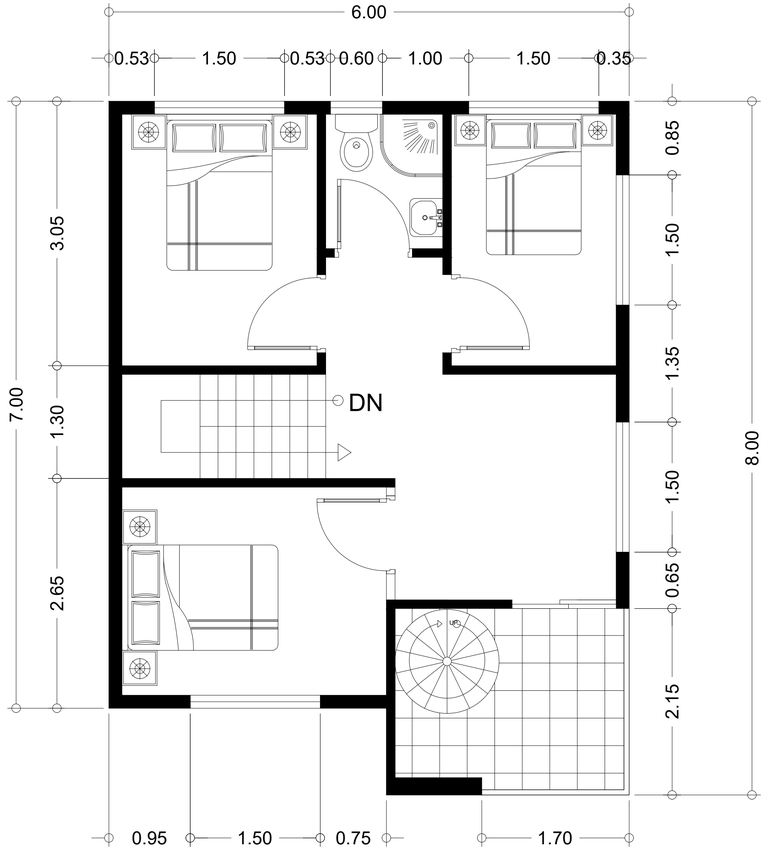

2 A–2 SECOND FLOOR PLAN
SCALE 1:75MTS

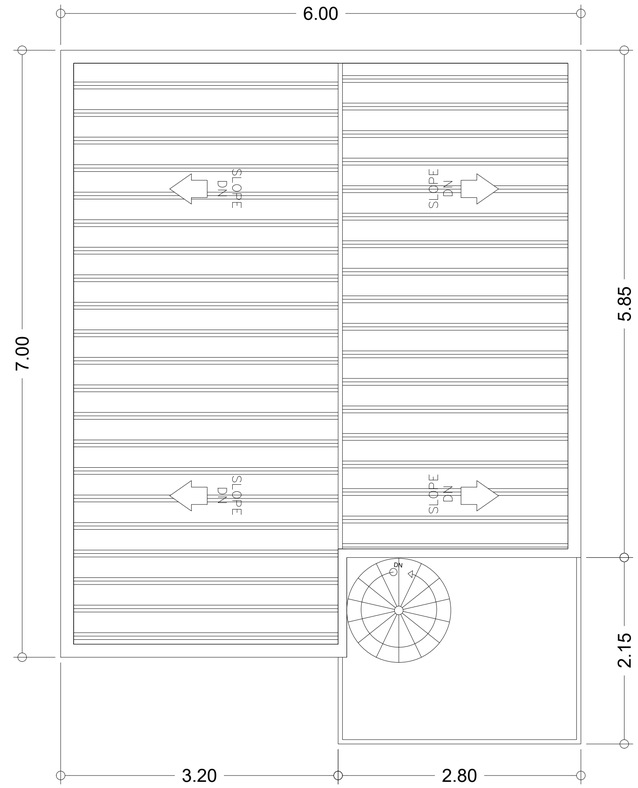

3 A–2 ROOF/DECK FLOOR PLAN
SCALE 1:75MTS

DESIGN CONSULTANT: ARCHITECT		DESIGN CONSULTANT: ENGINEER	
PTR NO.	REG. NO.	PTR NO.	REG. NO.
ISSUED ON	TIN.	ISSUED ON	TIN.
PLACE		PLACE	

DESIGN BY:
CHECKED BY:
DRAWN BY: MCPB
DATE:

IMPORTANT:
THESE DRAWINGS ARE INTELLECTUAL PROPRIETARY RIGHTS RETAINED BY DESIGNER OVER ANY DESIGNERS DOCUMENTS UNLESS THERE IS A WRITTEN STIPULATION TO THE CONTRARY. COPYRIGHT IN A WORK OF DESIGNER.
(RA 544)


PROJECT:
PROPOSED TWO-STOREY RESIDENTIAL W/ ROOFDECK
LOCATION :

OWNER
SHEET CONTENTS:


REVISIONS:

SHEET NO: A-2

☐ DESIGN DEVELOPMENT ■ FOR PERMIT PLAN ☐ FOR CONSTRUCTION PLAN ☐ ADDENDUM PLAN ☐ AS-BUILT PLAN

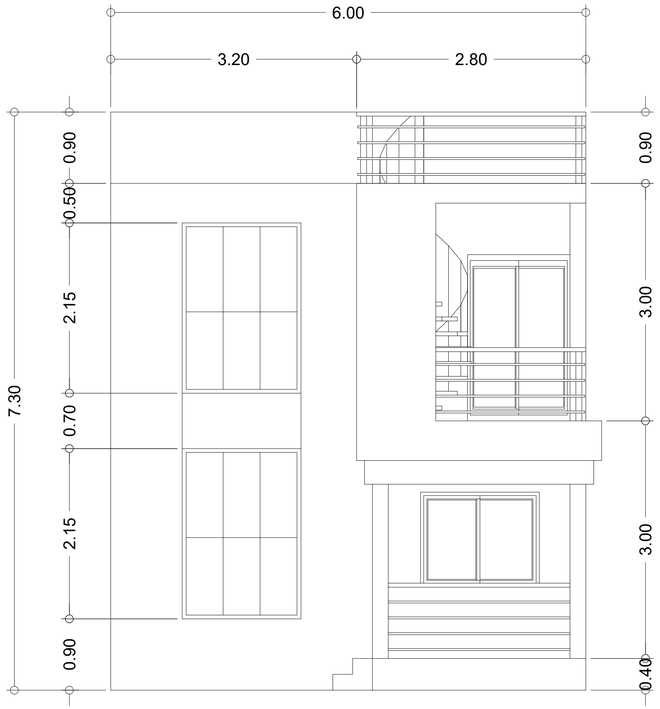

1 / A–3 FRONT ELEVATION
SCALE 1:75MTS

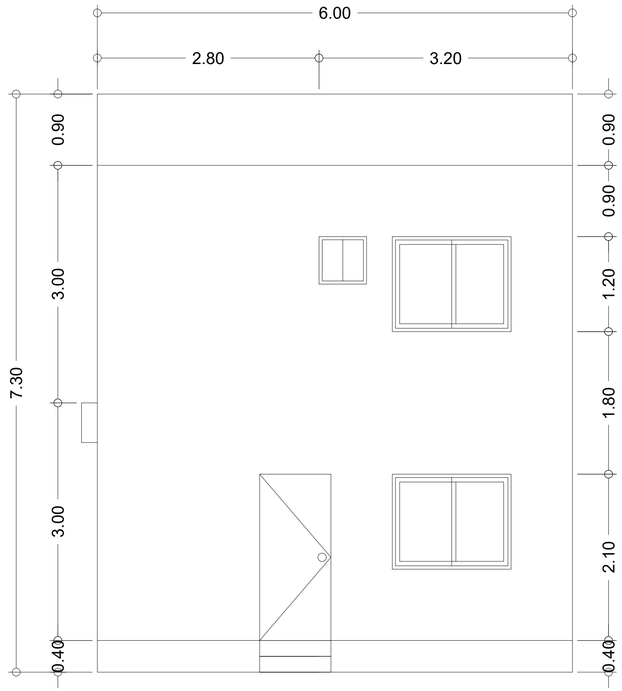

1 / A–3 REAR ELEVATION
SCALE 1:75MTS



1 / A–3 RIGHT SIDE ELEVATION
SCALE 1:75MTS

DESIGN CONSULTANT: ARCHITECT		DESIGN CONSULTANT: ENGINEER	
PTR NO.	REG. NO.	PTR NO.	REG. NO.
ISSUED ON	TIN.	ISSUED ON	TIN.
PLACE		PLACE	

DESIGN BY:
CHECKED BY:
DRAWN BY: MCPB
DATE:

IMPORTANT:
THESE DRAWINGS ARE INTELLECTUAL PROPRIETARY RIGHTS RETAINED BY DESIGNER OVER ANY DESIGNERS DOCUMENTS UNLESS THERE IS A WRITTEN STIPULATION TO THE CONTRARY. COPYRIGHT IN A WORK OF DESIGNER.
(RA 544)

PROJECT:
PROPOSED TWO-STOREY RESIDENTIAL W/ ROOFDECK
LOCATION :

OWNER
SHEET CONTENTS:

REVISIONS:

SHEET NO: A-3

☐ DESIGN DEVELOPMENT ■ FOR PERMIT PLAN ☐ FOR CONSTRUCTION PLAN ☐ ADDENDUM PLAN ☐ AS-BUILT PLAN